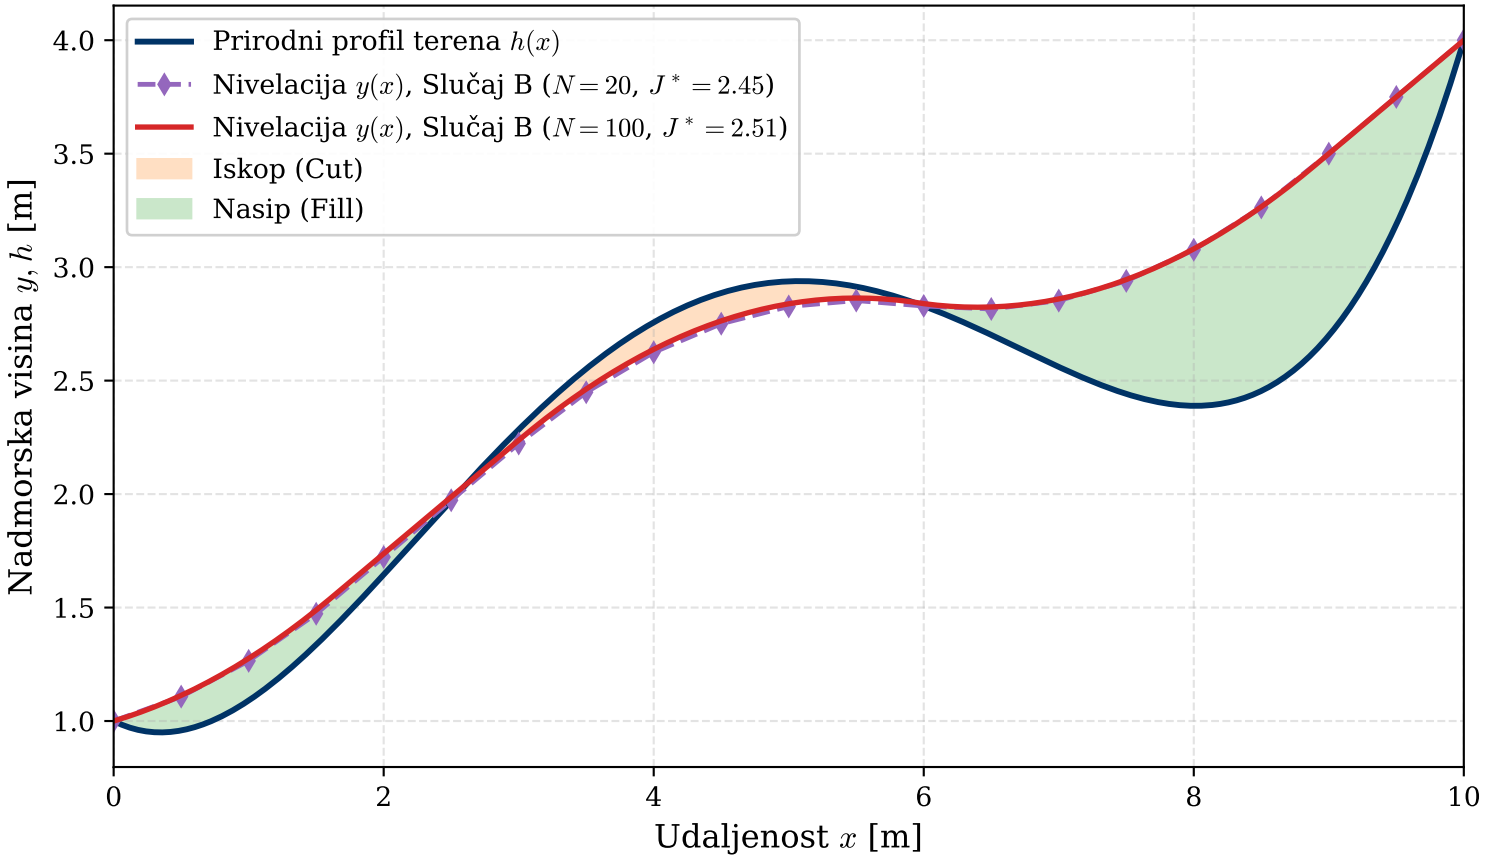
Zadatak 3: Optimalni uzdužni profil ceste — Slučaj B ($b_1 = 0.5, b_2 = 0.2$)
Prirodni profil terena $h(x)$
Nivelacija $y(x)$, Slučaj B ($N = 20$, $J^* = 2.45$)
Nivelacija $y(x)$, Slučaj B ($N = 100$, $J^* = 2.51$)
Iskop (Cut)
Nasip (Fill)
Nadmorska visina y, h [m]
Udaljenost x [m]
1.0
1.5
2.0
2.5
3.0
3.5
4.0
0
2
4
6
8
10